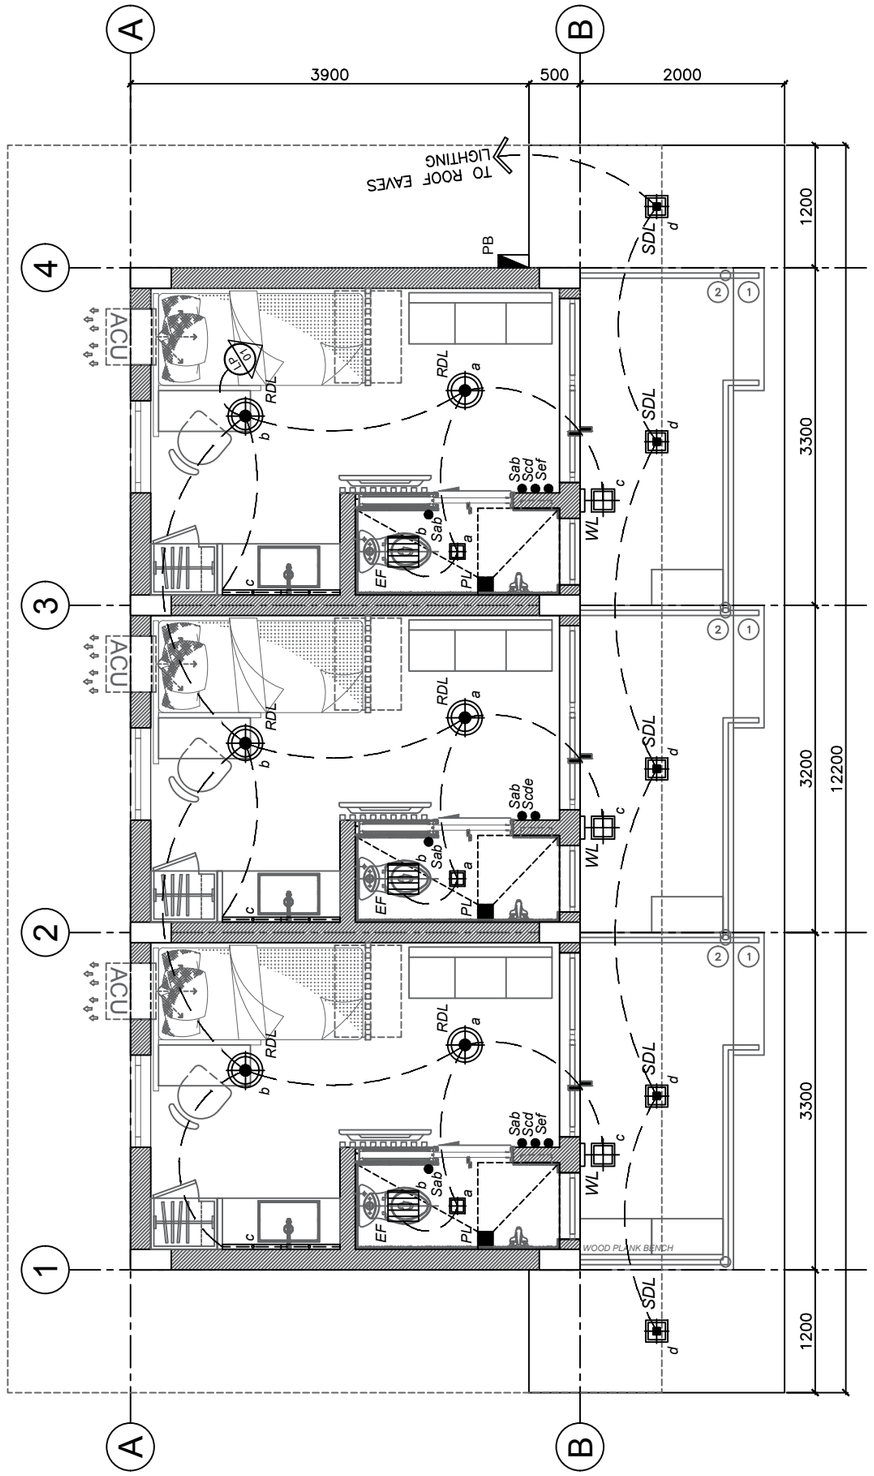

PROPOSED LIGHTING LAYOUT 1
1:60 MTS
SCALE:
1 E-200

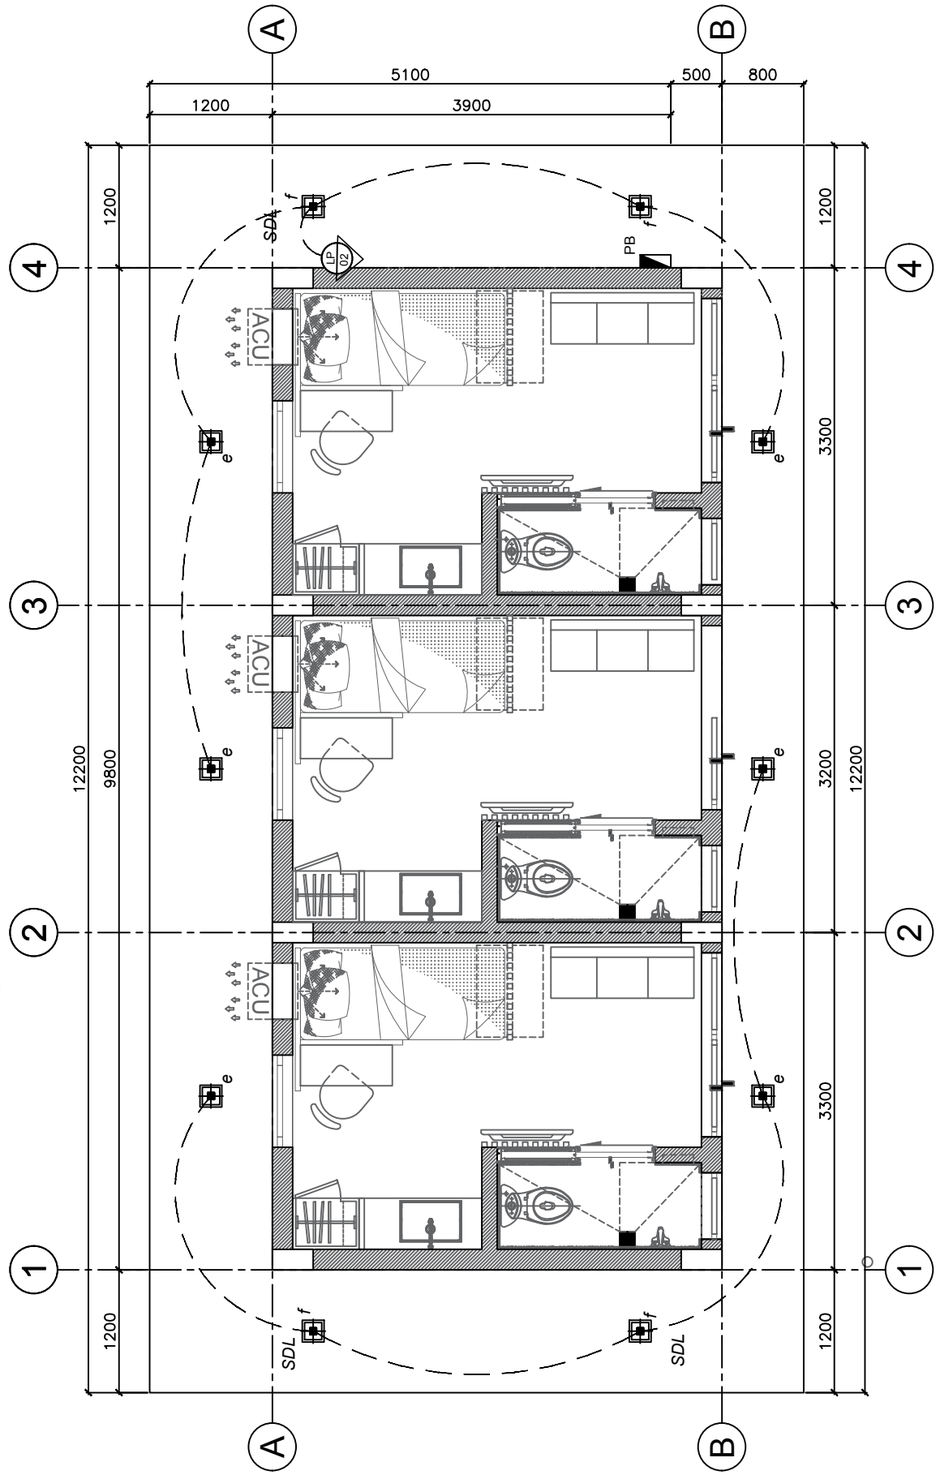

PROPOSED ROOF LIGHTING LAYOUT 2
1:60 MTS
SCALE:
2 E-200

LIGHTING FIXTURES	
SYMBOL	DISCRIPTION
	RECESSED L.E.D. DOWNLIGHT(12W)
	SURFACE-MOUNTED L.E.D. DOWNLIGHT(25W)
	RECESSED L.E.D. DOWNLIGHT (25W)
	L.E.D. WALL LIGHT (15W)
	L.E.D. STRIP LIGHT
S_{abc}	SWITCHES
S_3	3 WAY SWITCH

REPUBLIC OF THE PHILIPPINES
DEPARTMENT OF SOCIAL WELFARE AND DEVELOPMENT
PRK. BUMANAAG, BRGY.ZONE III,
KORONADAL CITY, SOUTH COTABATO, FO XII

PREPARED BY:
ENGR. CRESSYL ANN E. BANTAYA
TECHNICAL FACILITATOR

CHECKED BY:
ENGR. FRANCIS C. ESTOMATA
PDO III

RA 9266 SECTION 33
Drawings and specifications and other contract documents duly signed, stamped or sealed, as instruments of service, are the intellectual property and documents of the architect, whether the object for which they are made is executed or not. It shall be unlawful for any person to duplicate or make copies of said documents for use in the repetition of and for other projects or buildings, whether executed partly or in whole, without the written consent of the architect or author of said documents.

REVIEWED AND VERIFIED BY:
ENGR. ROLLY A. TEOFILO
PDO IV FOR INFRA

PROJECT TITLE:
CONSTRUCTION OF 2-UNITS ISOLATION BUIDLING (11-ROOMS)

LOCATION:
RRCY, BRGY. BUKAY PAIT, TANTANGAN, SOUTH COTABATO

APPROVED BY:
CEZARIO JOEL C. ESPEJO
REGIONAL DIRECTOR
DSWD - FIELD OFFICE XII

SHEET CONTENT
LIGHTING LAYOUT

REVISIONS		
MARK	DATE	

PROJECT NO.	
DRAWN BY :	CEB
DESIGNED BY :	
DATE :	--
CHECKED BY :	FCE

SHEET NO.
E-200

SCALE A3 AS SHOWN
A1