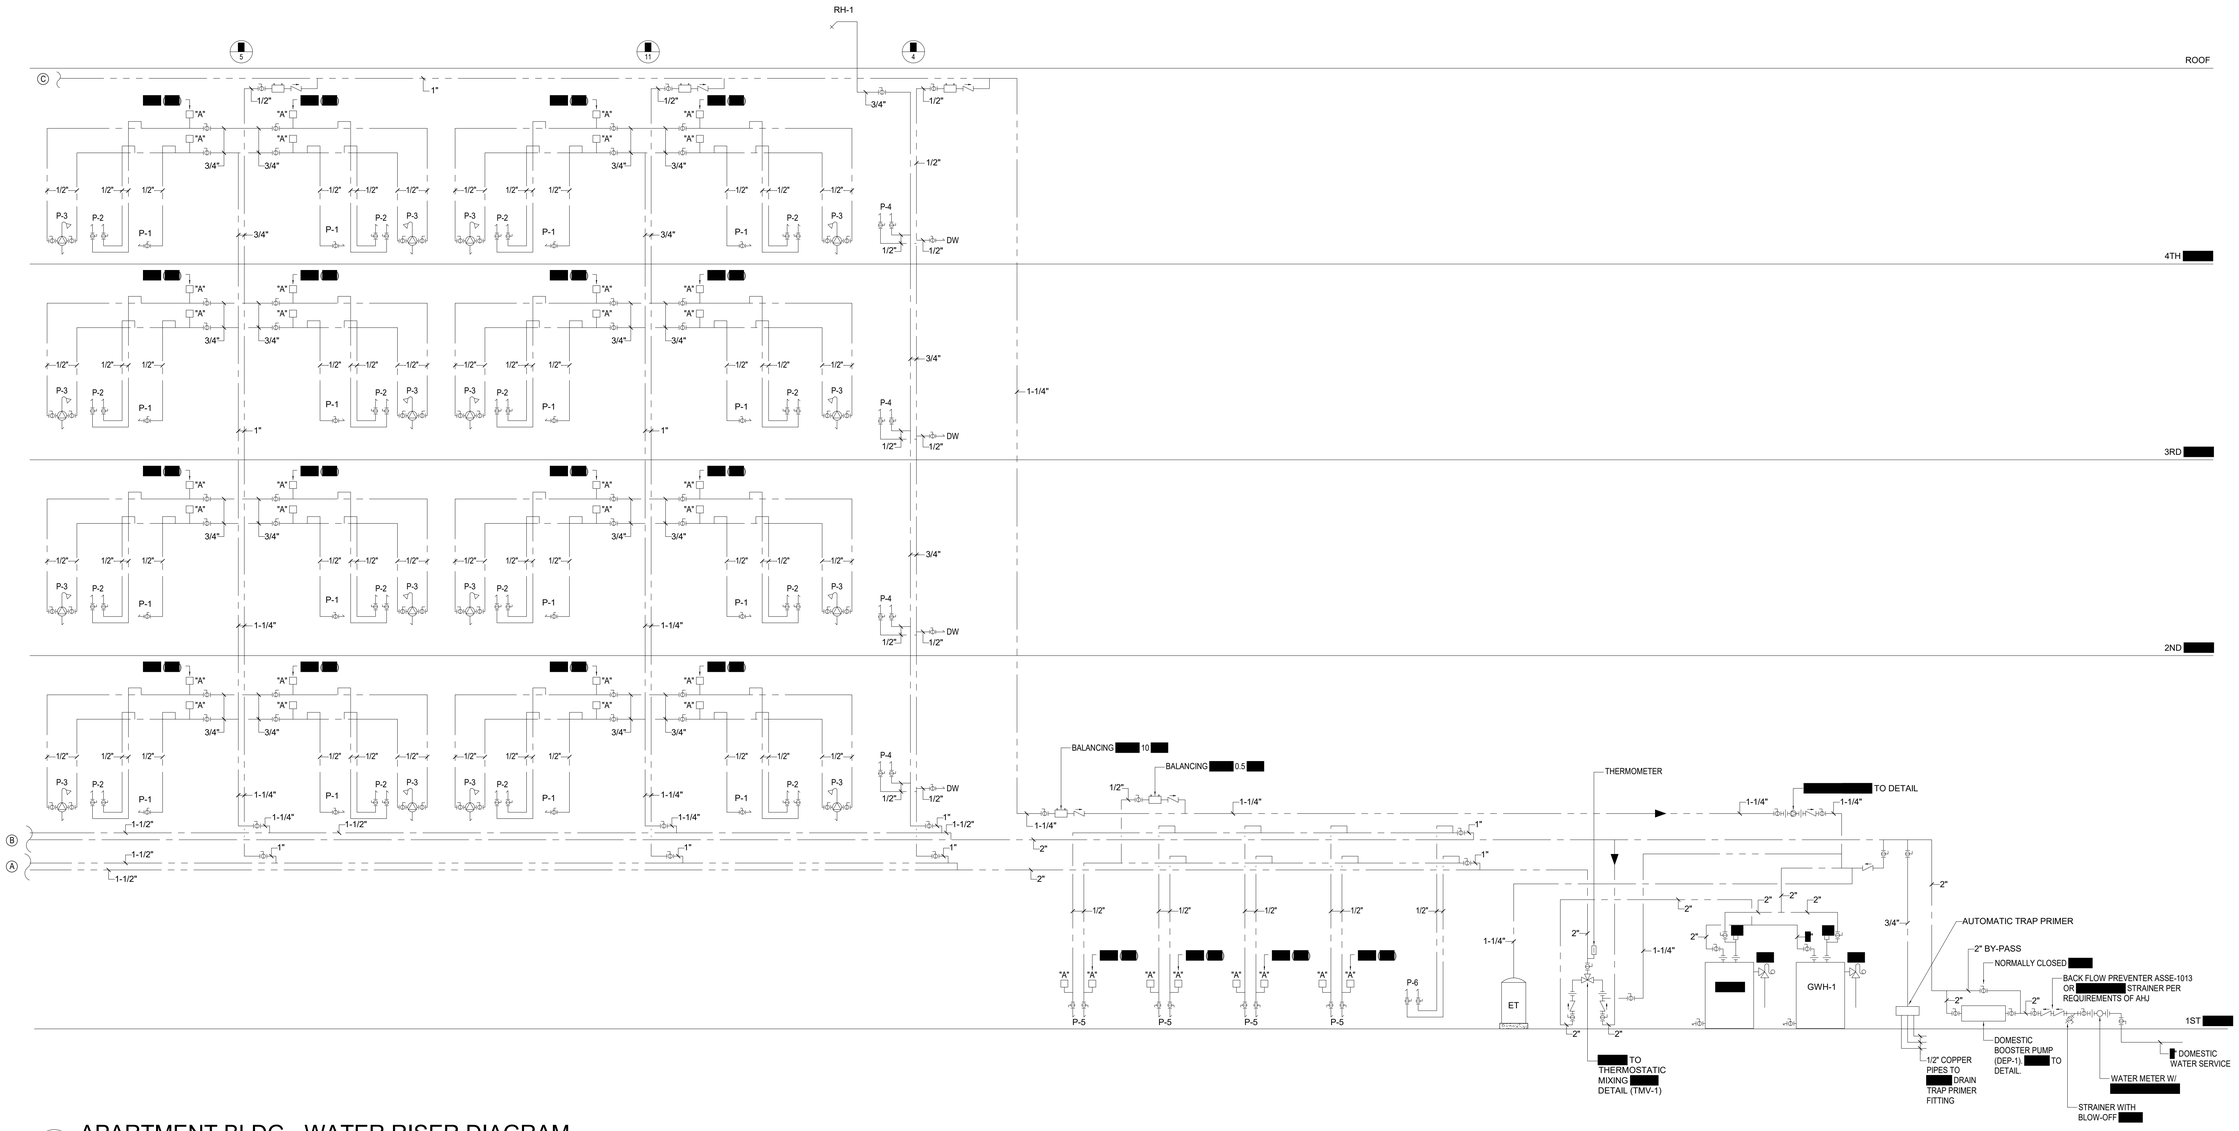

1 APARTMENT BLDG - WATER RISER DIAGRAM

NTS

REVISION	DESCRIPTION	BY	DATE

ARCHITECT

[redacted]

NIST

FOR OFFICIAL USE ONLY

[redacted]

NIST – MID RISE APARTMENT

PLUMBING RISERS

P501

SH. NO. ___ OF ___ [redacted]. P501

APPROVED BY	DATE	SPONSOR	DATE	MAINTENANCE [redacted] OFF.	[redacted]	[redacted]	DATE	SHED – NIST FIRE MARSHAL/AHJ	[redacted]	FACILITIES [redacted]R. OFF.	DATE	VAY [redacted]	DATE	AA DRAWN BY	DATE	08/15/2022 PROJECT/ W.O. #	Project [redacted]