PRODUCED BY AN AUTODESK STUDENT VERSION

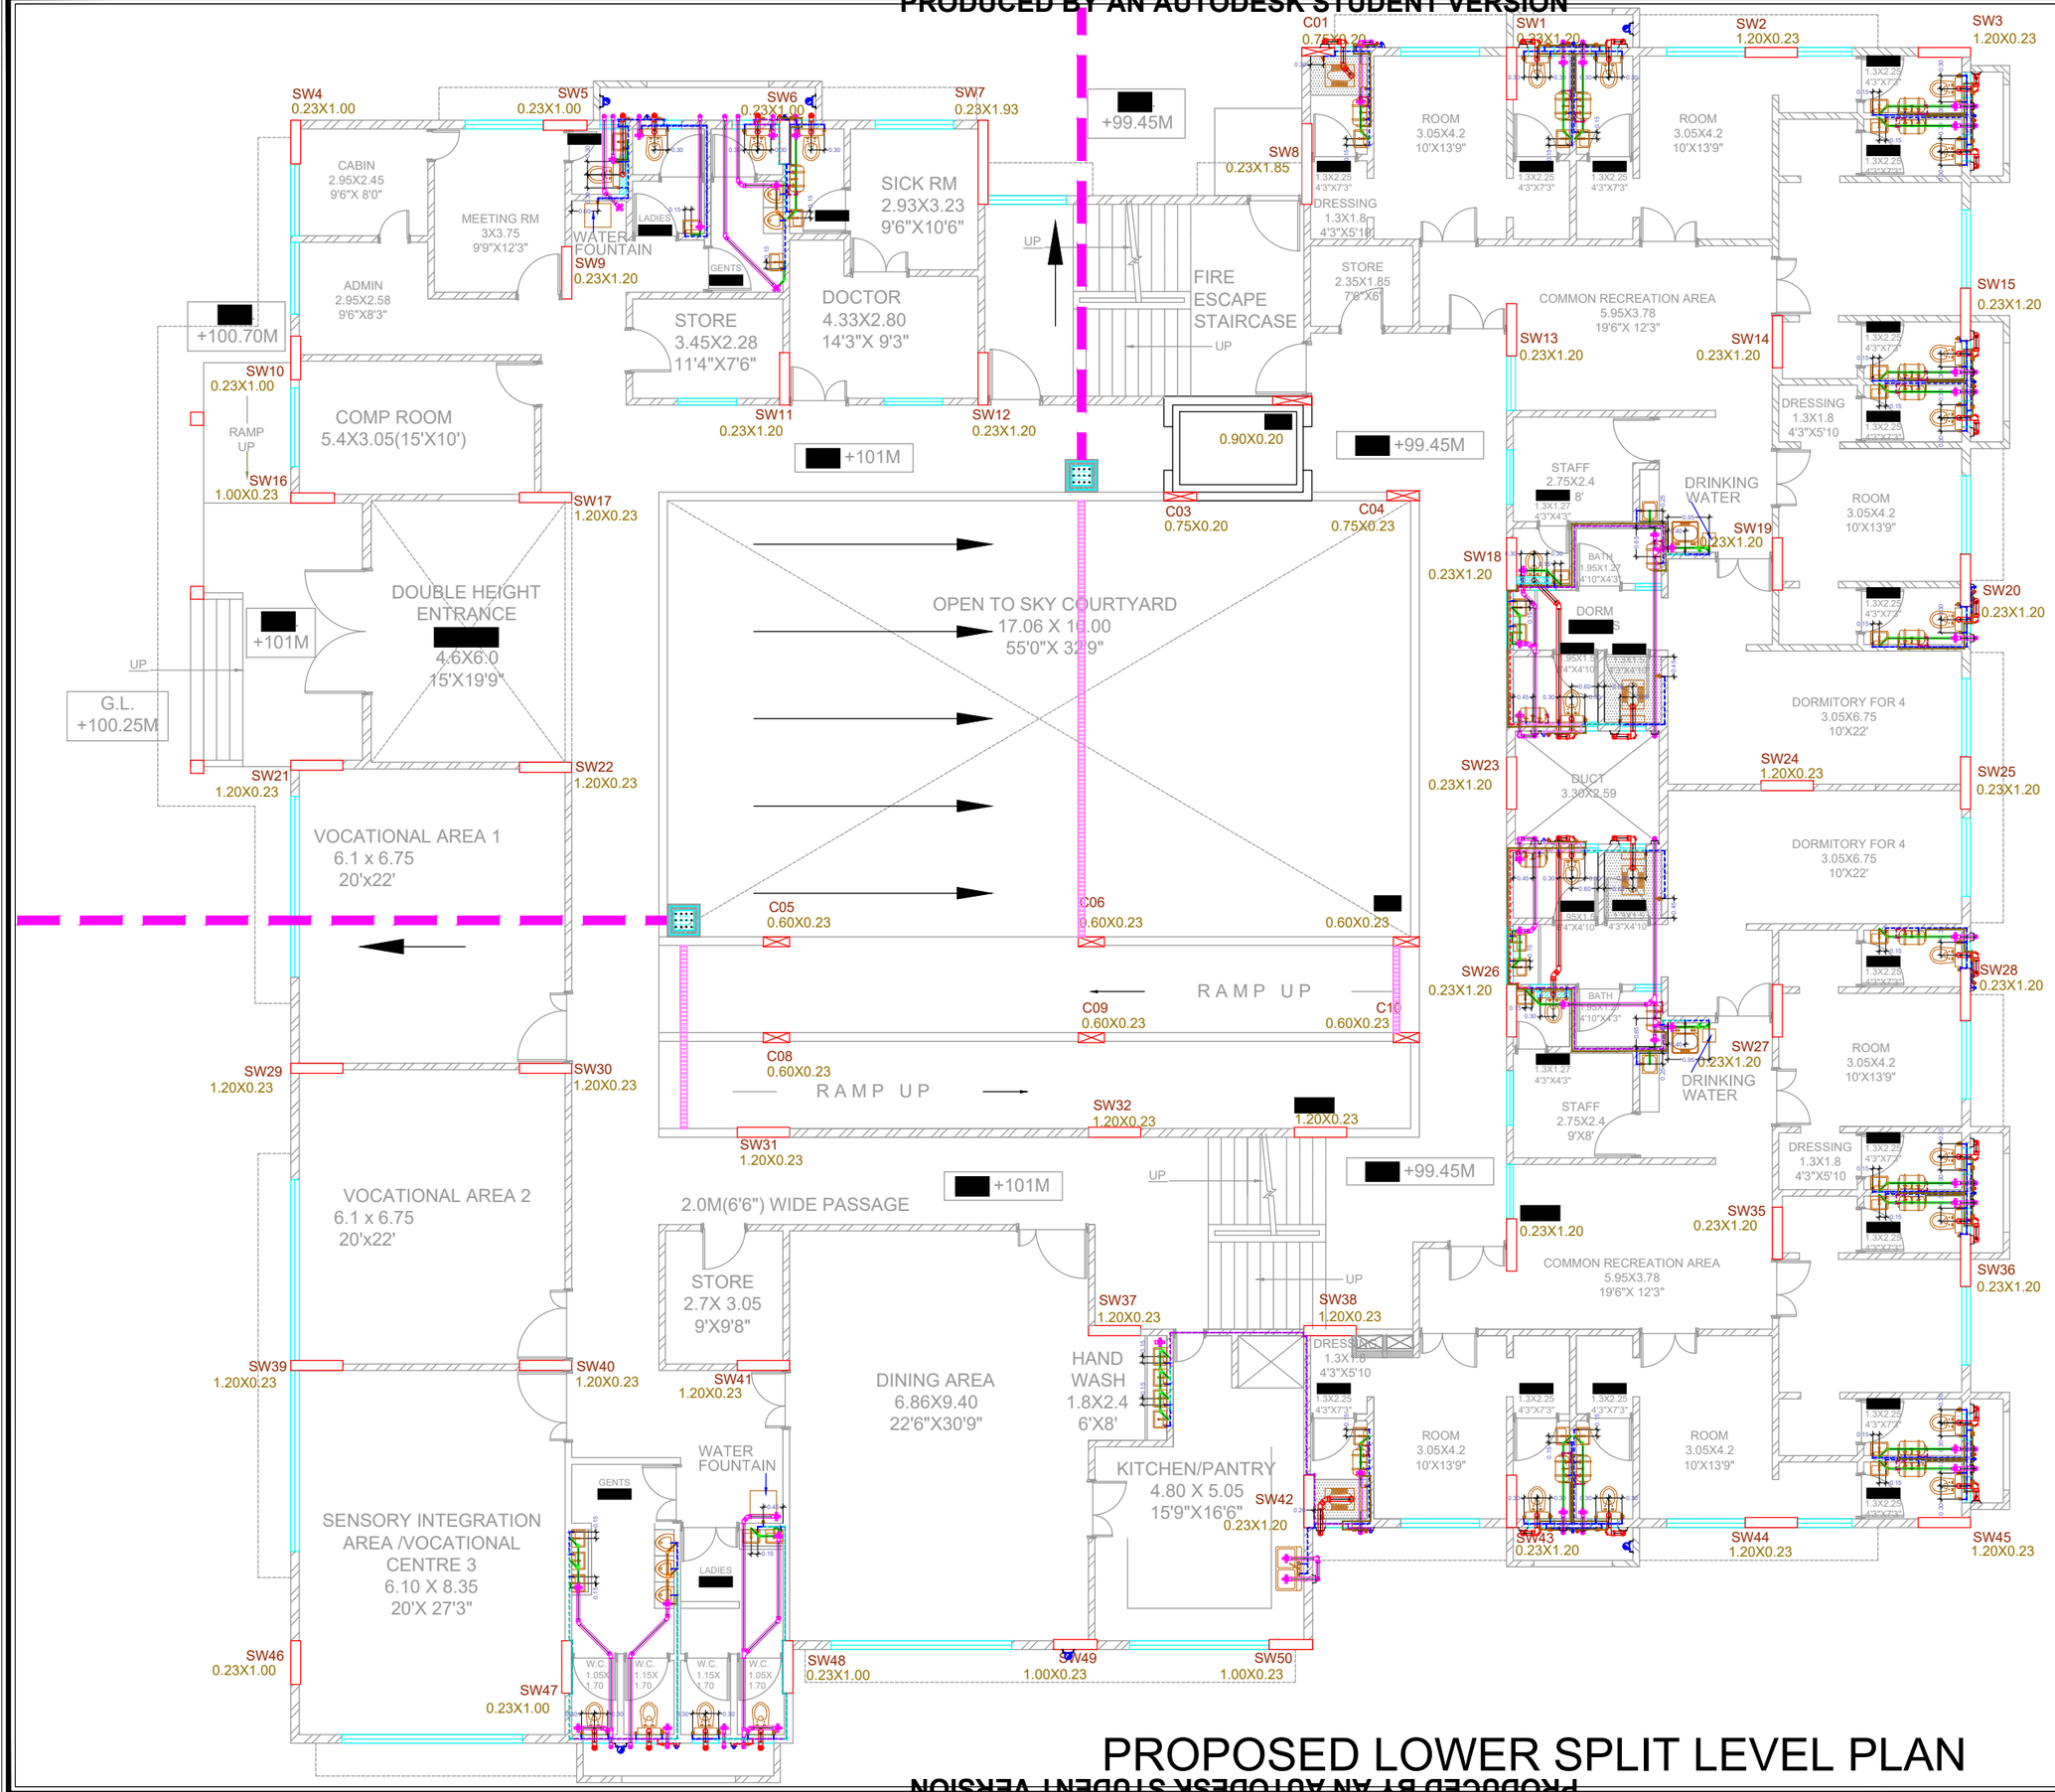

PROPOSED LOWER SPLIT LEVEL PLAN

DRG NO.	M/167/04 R5	02/03

[redacted]

McLIN Consultants Pvt. Ltd. ADVANCE COPY Pune-30

NOTES:

	SOIL PIPE ([redacted] 'B' TYPE) Ø 110 mm
	WASTE PIPE ([redacted] 'B' TYPE) Ø 75 mm
	WASTE PIPE ([redacted] 'B' TYPE) Ø 50 mm
	WASTE PIPE ([redacted] 'B' TYPE) Ø 40 mm
CWS	CPVC [redacted] 11 DOMESTIC WATER LINE Ø 40 mm
CWS	CPVC [redacted] 11 DOMESTIC WATER LINE Ø 32 mm
CWS	CPVC [redacted] 11 DOMESTIC WATER LINE Ø 25 mm
CWS	CPVC [redacted] 11 DOMESTIC WATER LINE Ø 20 mm
CWS	CPVC [redacted] 11 DOMESTIC WATER LINE Ø 15 mm
HW	CPVC [redacted] 11 [redacted] Ø 15 mm
	KiTEC COMPOSITE SOLAR [redacted] Ø 12-16 MM
	[redacted] FLOOR TRAP
	SHOWER WITH MIXER
	BIB COCK WITH HEALTH FAUCET
	ANGULAR STOP COCK
	BALL VALVE
	NON RETURN VALVE
	BOILER
	WALL MOUNTED EWC WITH FLUSH TANK
	WASH BASIN
	URINAL
	LEDGE WALL
	[redacted] MAKE PRECAST DRAIN
	[redacted]
	[redacted] CHAMBER 450 X 450MM

REV	DATE	REMARK / SUBJECT
R5	02.04.21	REVISED ARCH. PLAN
R4	28.12.19	REVISED ARCH. PLAN
R3	27.11.19	REVISED ARCH. PLAN
R2	19.11.19	REVISED ARCH. PLAN
R1	03.10.19	EWC LOCATION CHANGE

REVISIONS

DRAWING TITLE	LOWER SPLIT LEVEL PLUMBING DETAILS FLOOR PLAN
PROJECT	[redacted]
	McLIN CONSULTANTS PVT.LTD. [redacted] IN PLUMBING AND ENVIRONMENTAL ENGINEERING [redacted] 5, [redacted] Pune - 411 030 Tel - 2432 0010 e-mail - [redacted]
CLIENT	[redacted] SUBHASH LELE
ARCHITECT	INDESIGN ARCHITECTS
NORTH	DATE:- 01.10.2019
	DRAWN BY PANKAJ G.
	CHECKED BY MOHANISH P.
	APPROVED BY MOHANISH P.
SCALE:-NTS	

[redacted] Plumbing Drawings (1)\ARC Plumbing Drawings\R5 [redacted] Details 02.04.21.dwg

PRODUCED BY AN AUTODESK STUDENT VERSION