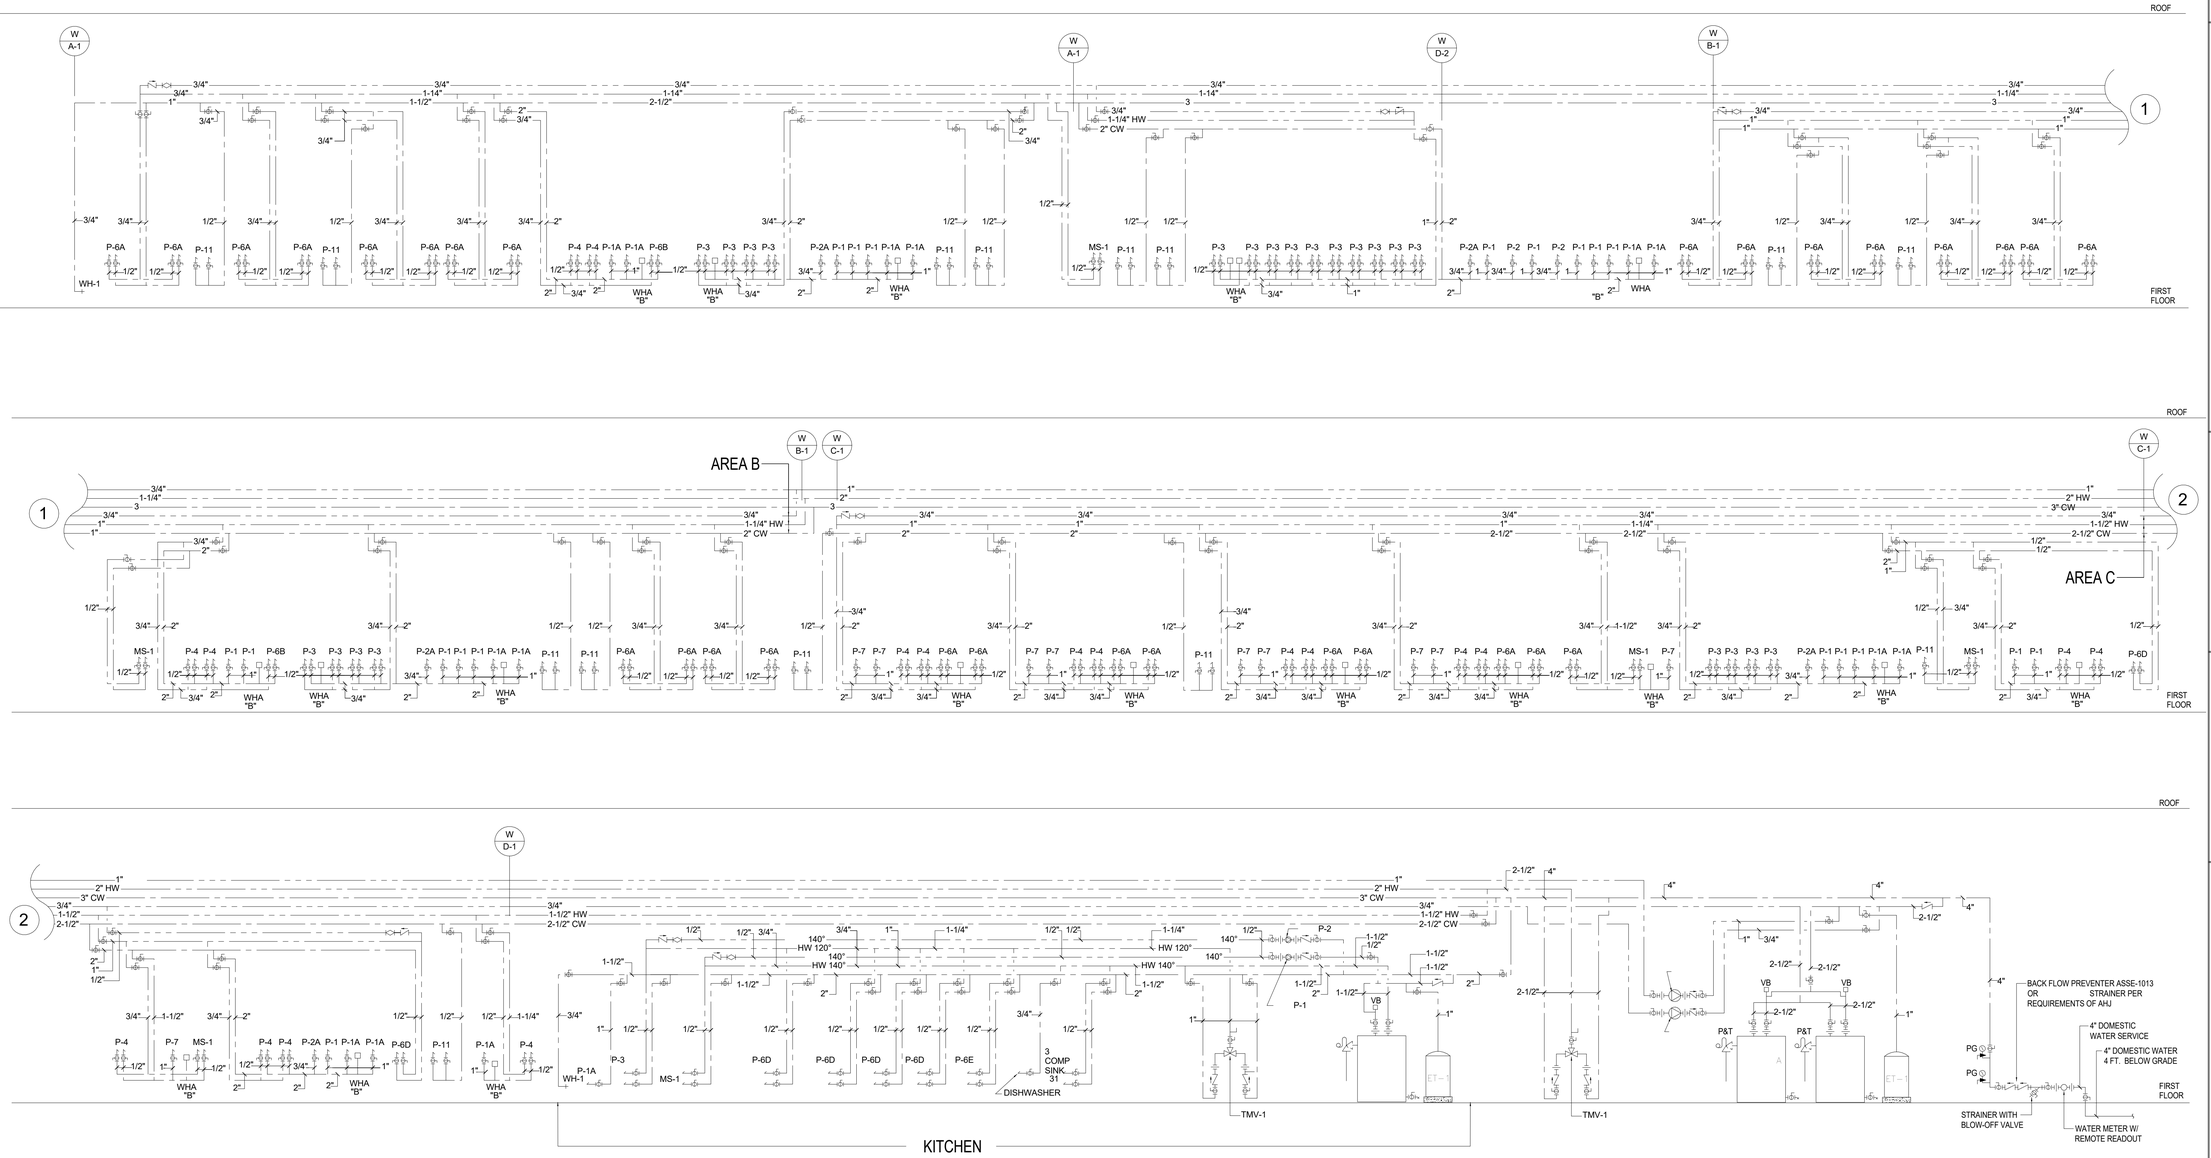

1 SCHOOL WATER RISER DIAGRAM
1/4" = 1'-0"

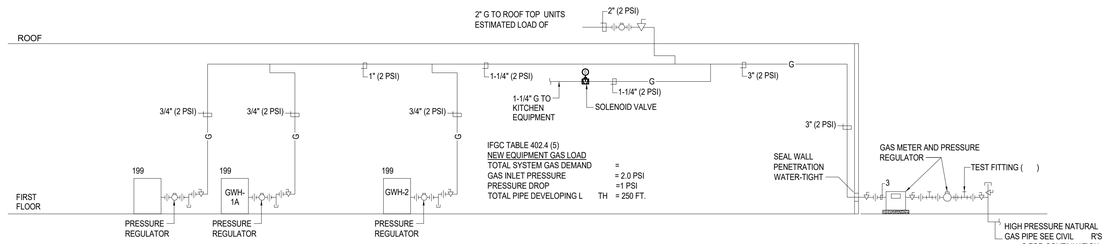

2 SCHOOL GAS RISER DIAGRAM
1/4" = 1'-0"

	DESCRIPTION	BY	DATE

ARCHITECT

MEP.

FOR OFFICIAL USE ONLY

NIST – PRIMARY SCHOOL

PLUMBING WATER & GAS RISER DIAGRAM

P502

SH. NO. ____ OF ____ . P502

APPROVED BY	DATE	SPONSOR	DATE	MAINTENANCE . OFF.	DATE		DATE	SHED – NIST FIRE MARSHAL/AHJ	FACILITIES R. OFF.	DATE	VAY PROJECT LEADER	DATE	AA DRAWN BY	DATE	08/15/2022 PROJECT/ W.O. #	Project Number