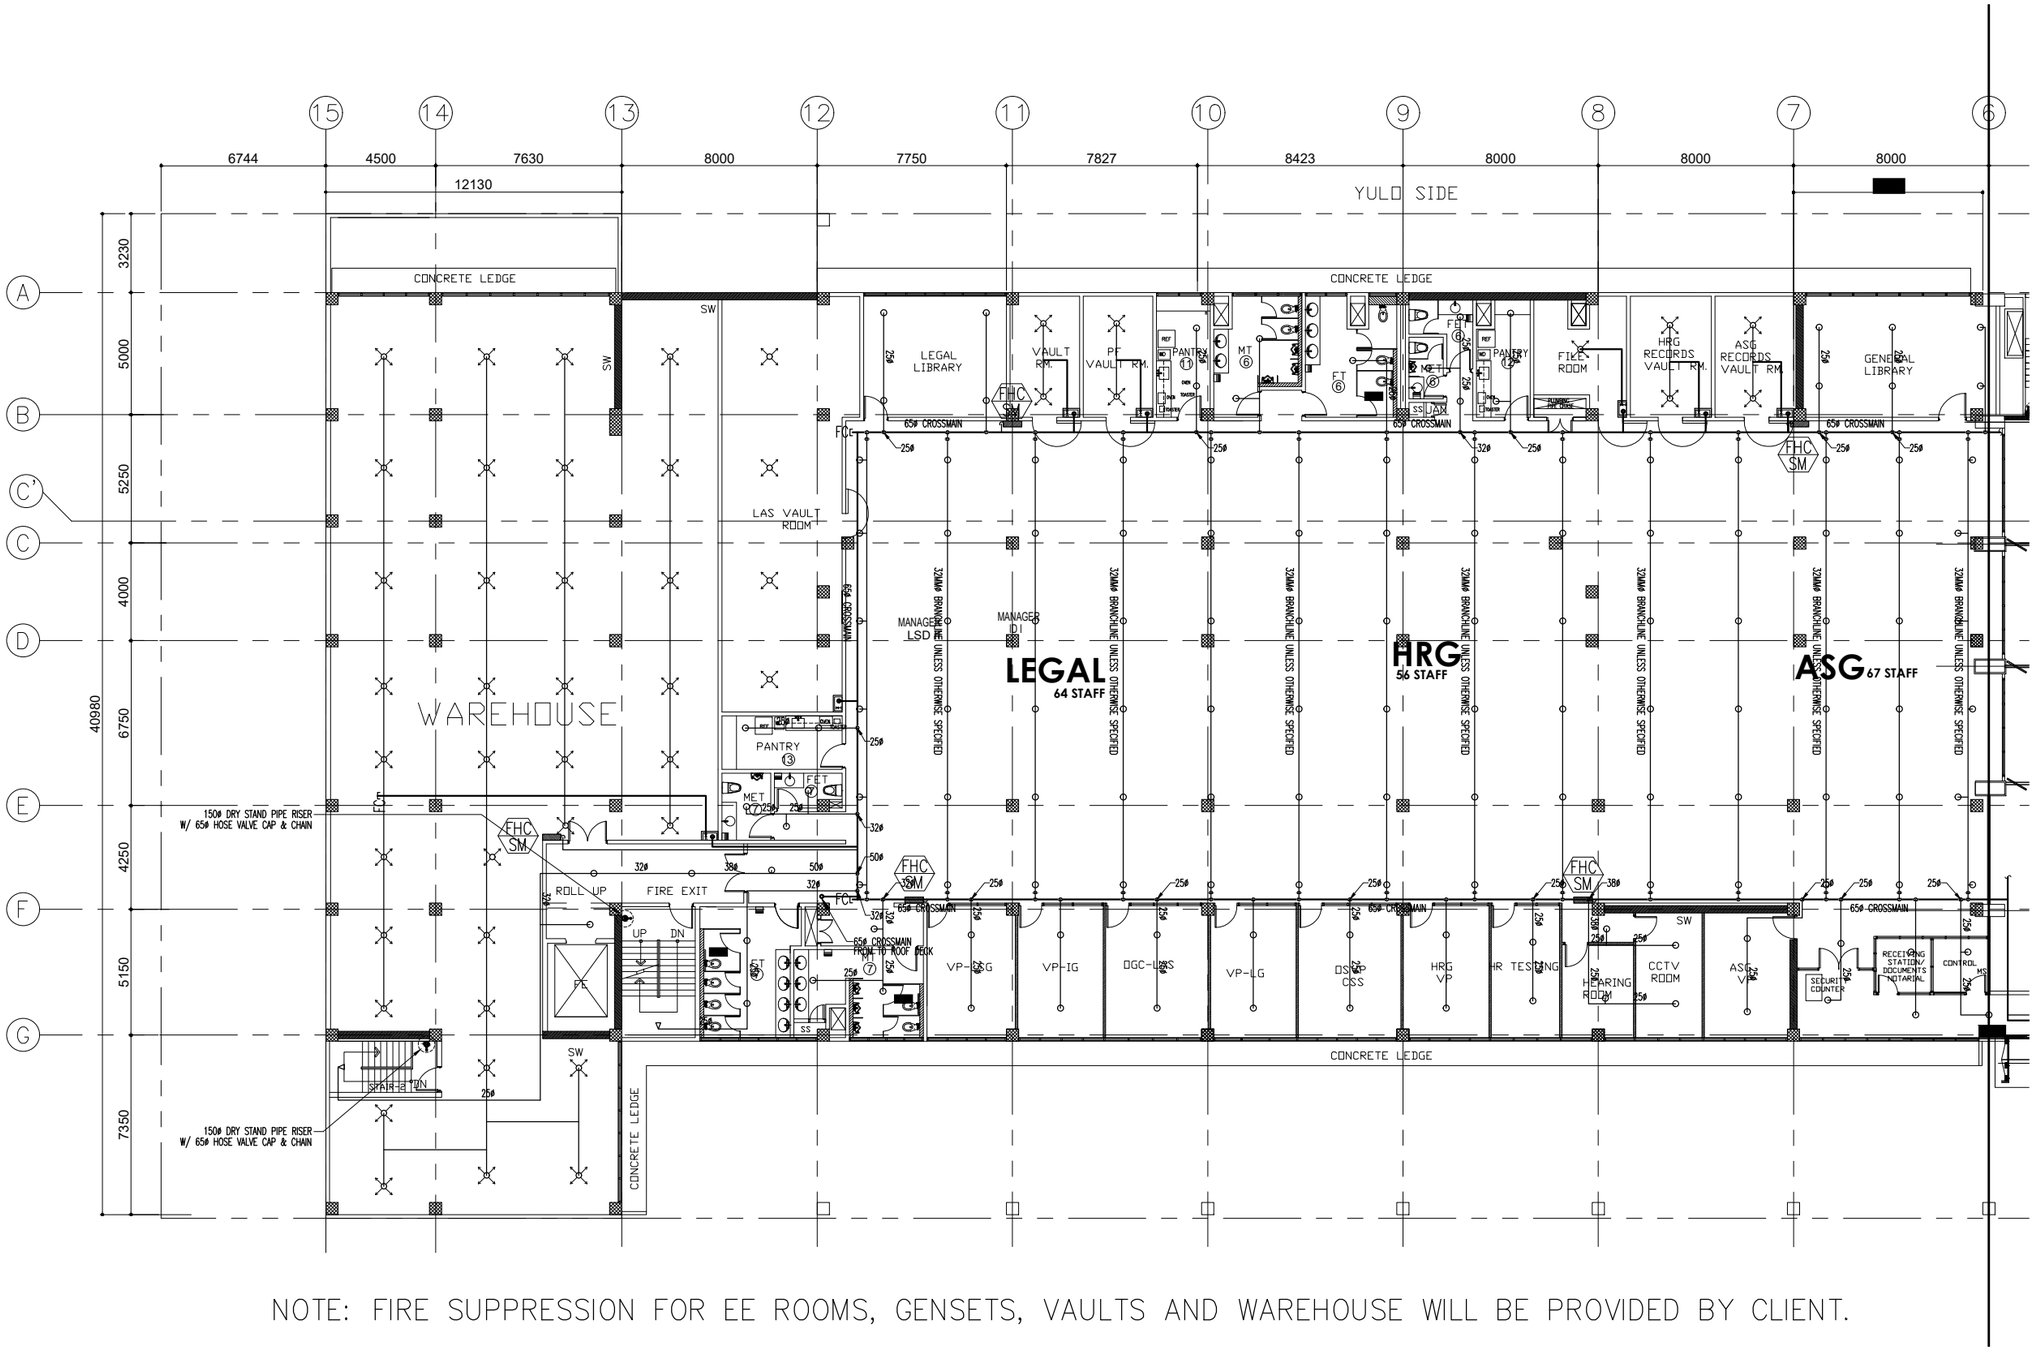

NOTE: FIRE SUPPRESSION FOR EE ROOMS, GENSETS, VAULTS AND WAREHOUSE WILL BE PROVIDED BY CLIENT.

A FP-06 [redacted] SCALE 1:100

GRAPHIC SCALE: 0 2 4 6 8
SCALE 1:100 M
NOTE: CHECK GRAPHIC SCALE PRIOR TO SCALING

CONSULTANT		OWNER	APPROVED BY:	PROJECT TITLE	SHEET CONTENT/S :	ISSUE NO.	REVISIONS	NO.	DATE		DATE	SHEET NO.
[redacted], CO. ENGINEERS * PLANNERS * CONSULTANTS 3431 GUERNICA ST., PALANAN, MAKATI CITY [redacted] Nos. 8317115, 8337030	RAMON D. AGUILOS PROFESSIONAL MECHANICAL ENGINEER PTR NO.: 2464195 D PRC NO. : 2736 DATE : 01-05-22 TIN. NO. : 137-133-799 PLACE : QUEZON CITY	PDIC	[redacted] VICE PRESIDENT ADMINISTRATIVE SERVICES GROUP	RENOVATION OF [redacted] CHINO ROCES LOCATION: 2228 [redacted] MAKATI CITY	FIFTH FLOOR PLAN [redacted]					DESIGNED BY: RDAEC		FP-06
										CADD BY: RJA		
										CHECKED BY:		
										APPROVED BY:		
										SCALE:	AS SHOWN	