© [redacted] AND PARKER, P.C. 2014

SHEET KEY NOTES

1. EMERGENCY STORM DRAIN DISCHARGE TO GRADE PIPE 18"-24" ABOVE FINISHED GRADE. PROVIDE DISCHARGE NOZZLE WITH SCREEN. COORDINATE WITH CIVIL PLANS FOR GRADE ELEVATION.
2. PROVIDE ACCESS PANELS TO ALL DOMESTIC SUPPLY VALVES.
3. PROVIDE ACCESS PANELS TO ALL WATER HAMMER ARERESTORS. REFER TO PLUMBING RISER DIAGRAM FOR WATER HAMMER ARRESTOR LOCATION.

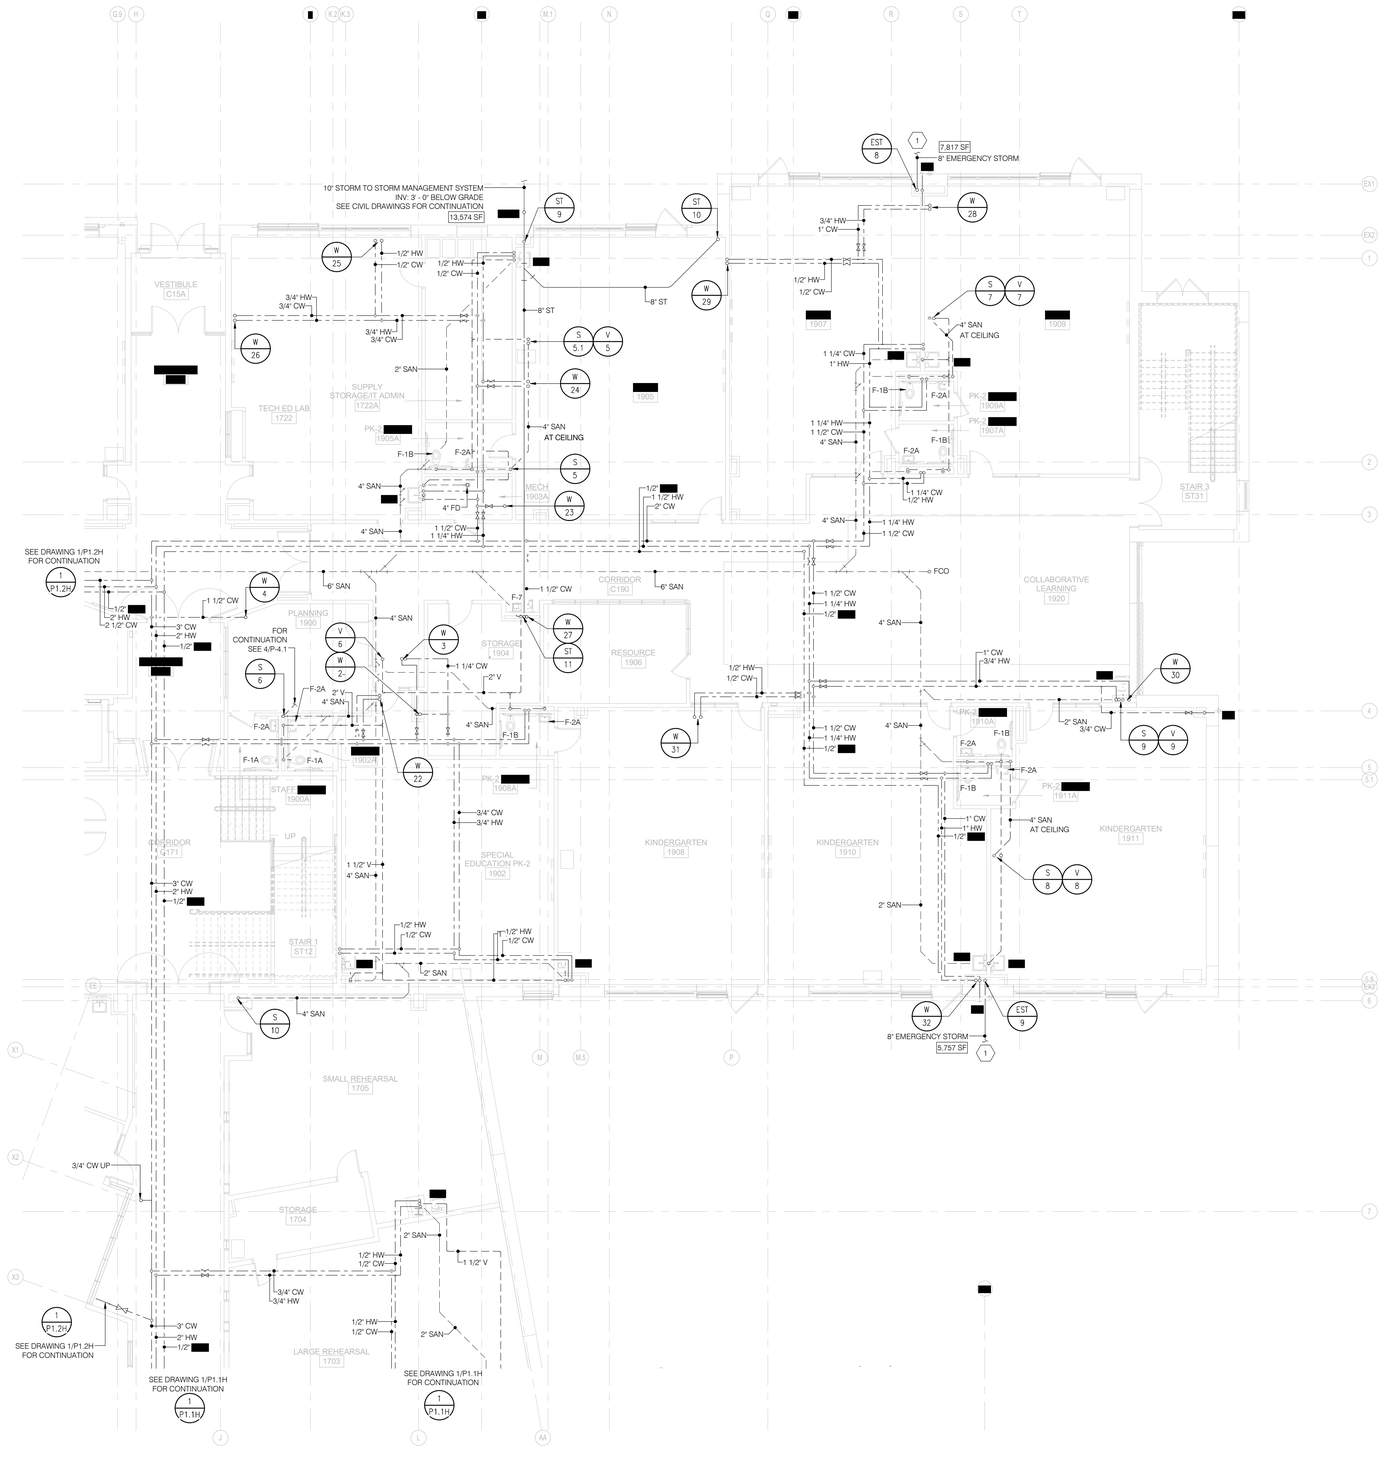

1 / P-1.3H PLUMBING PARTIAL FIRST FLOOR PLAN – AREA C
SCALE: 1/8" = 1'-0"

KEY PLAN

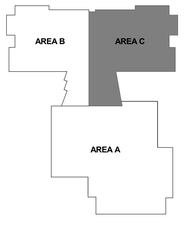

SETTY
ONE SOUTH STREET, SUITE 1110
BALTIMORE, MARYLAND 21202
[redacted] 410-539-5035
MASTER PLANNING • FACILITIES MANAGEMENT
ENERGY MANAGEMENT SERVICES • OPEN BUILDINGS
CAPITAL PROGRAM MANAGEMENT • CONSTRUCTION
DISTRICT OF COLUMBIA • MARYLAND
www.SETTY.com
PROJECT NUMBER: 2016-0117.0 0 0 0 0

11720 Beltsville Drive
Suite 600
Calverton, MD 20705
[redacted] 301.595.1000
www.[redacted]andparker.com

GRIMM AND PARKER

GP# 21553

PLUMBING PARTIAL FIRST FLOOR PLAN – AREA C

LAND

DATE	DESCRIPTION

P-1.3H

03/13/2017
BID SET

© [redacted] AND PARKER, P.C. 2014