[redacted] (LAST UPDATED 09/06/2024)

NOTE: SOME OF THE IN[redacted]ON PROVIDED HEREIN HAS BEEN DONATED BY OUR INDUSTRY PARTNERS ([redacted], HOLADAY-PARKS) IN ORDER TO EXPEDITE THE CREATION OF THESE SAMPLE PLANS. ANY INADVERTENT REFERENCE TO A SPECIFIC PROJECT IS PURELY COINCIDENTAL.

TIPS FOR USING EXAMPLE PLANS:

6X ← SEARCH THE [redacted] (CTRL+F) TO FIND A SPECIFIC PLA[redacted] VIEW DESIGN GUIDANCE REFERENCE.

? ← HOVER OVER [redacted]N MARK FOR ADDITIONAL IN[redacted]ION. DOUBLE-CLICK TO OPEN FULL [redacted]X.

NOTE: NOT ALL GUIDANCE ITEMS ARE CURRENTLY REFLECTED ON AVAILABLE EXAMPLE PLANS

CURRENT DESIGN GUIDANCE:
https://cdn.kingcounty.gov/-/media/king-county/depts/dph/documents/health-safety/environmental-health/pl[redacted]ing-gas-piping/plumbing-design-guidance.[redacted]

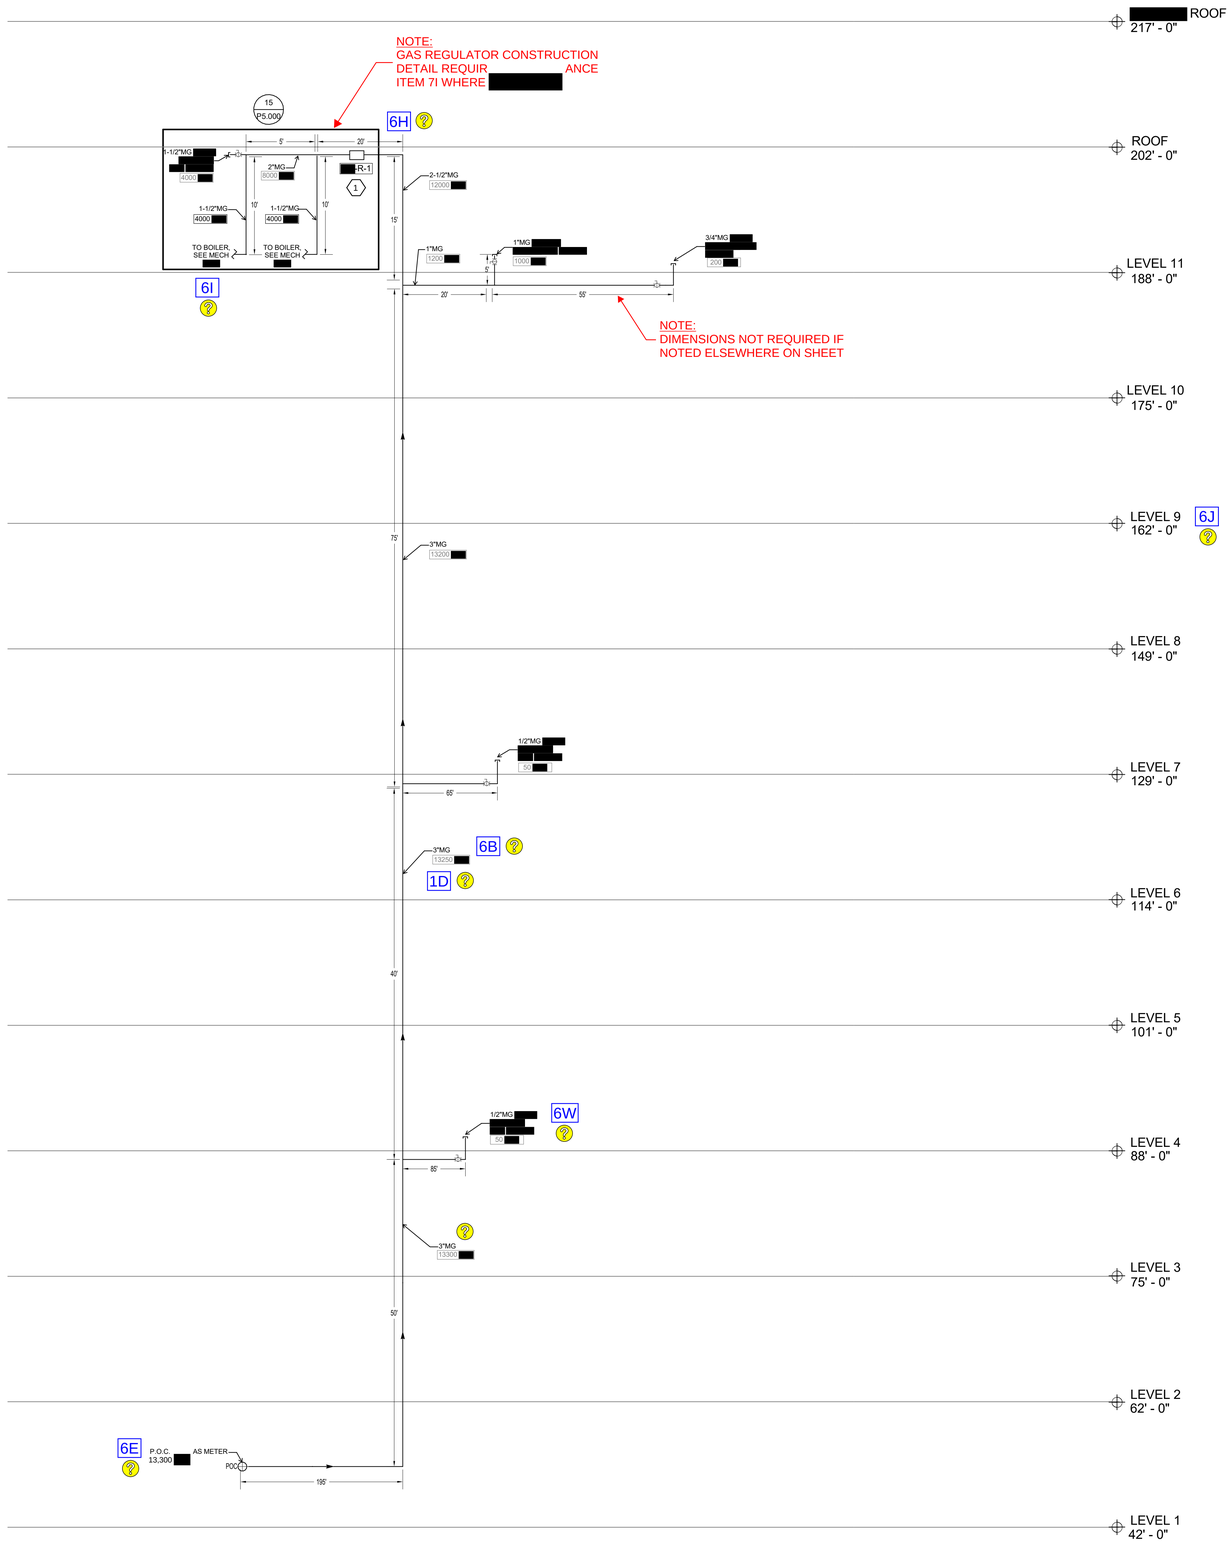

NATURAL GAS RISER DIAGRAM
SCALE: NTS

GENERAL NOTES

1. UNLESS OTHERWISE INDICATED, SYSTEM LOADING IS DENO[redacted]N CUBIC FEET PER HOUR OF NATURAL GAS. ([redacted]).
2. NATURAL GAS SYSTEM DESIGN BASED UPON IFGC/SFGC 402.4.3 'HYBRID PRESSURE' METHOD.
3. PIPE SIZING DOWNSTREAM OF PRESSURE REGULATORS BASED UPON IFGC/SFGC TABLE 402.4(2). PIPE SIZING UPSTREAM OF PRESSURE REGULATORS BASED UPON IFGC/SFGC TABLE 402.4(5).
4. EQUIVALENT L[redacted]F DELIVERY TO FURTHEST [redacted] 500'

KEYED NOTES

1. PRESSURE REGULATOR WITH LISTED VENT-LIMITING DEVICE PER IFGC/SFGC 410.3. INSTALLED IN CONTINUOUSLY VENTILATED MECHANICAL ROOM.

NOTE: T[redacted]PLE PLANS ARE NOT INTENDED TO MANDATE A SPECIFIC LAYOUT, [redacted] OR METH[redacted]. THESE PLANS ARE PROVIDED ONLY TO INDIC[redacted]TYPE OF IN[redacted]ON REQUIRED TO ENSURE AN EFFICIENT AND TIMELY PLAN[redacted]

PHSKC STAMP

ARCHITECT

NAME AND LOGO

CONTACT IN[redacted]ION

ENGINEERING FIRM

NAME AND LOGO

CONTACT IN[redacted]ION

ENGINEER OF RECORD

JOHN DOE
STATE OF WASHINGTON
REGISTERED PROFESSIONAL ENGINEER

DATE

EXAMPLE PROJECT
PROJECT ADDR[redacted], ZIP
PROJECT CITY, [redacted]

REVISION HISTORY

DATE	REV	ISSUE
DD/MM/YY	X	PERMIT ISSUE

DESIGNED BY:
DRAWN BY:

DRAWING ISSUE

PERMIT ISSUE

ISSUE DATE

SHEET TITLE

NATURAL GAS RISER DIAGRAM

SCALE: NTS

SHEET NUMBER

P5.31