GENERAL BASEMENT NOTES:

1. 1" WATER LINE REQUIRED TO ALL WATER HEATERS.
2. WATER HEATERS TO HAVE ENGINEERED SEISMIC CONNECTION STRAPS.
3. COMBUSTION AIR MUST ENTER FROM EXTERIOR OF MECHANICAL ROOM.
4. ALL [redacted]RETE BELOW FINAL GRADE MUST HAVE DAMP PROOFING.
5. 1 EGRESS LANDER REQUIRED IF NO OTHER EXIT.

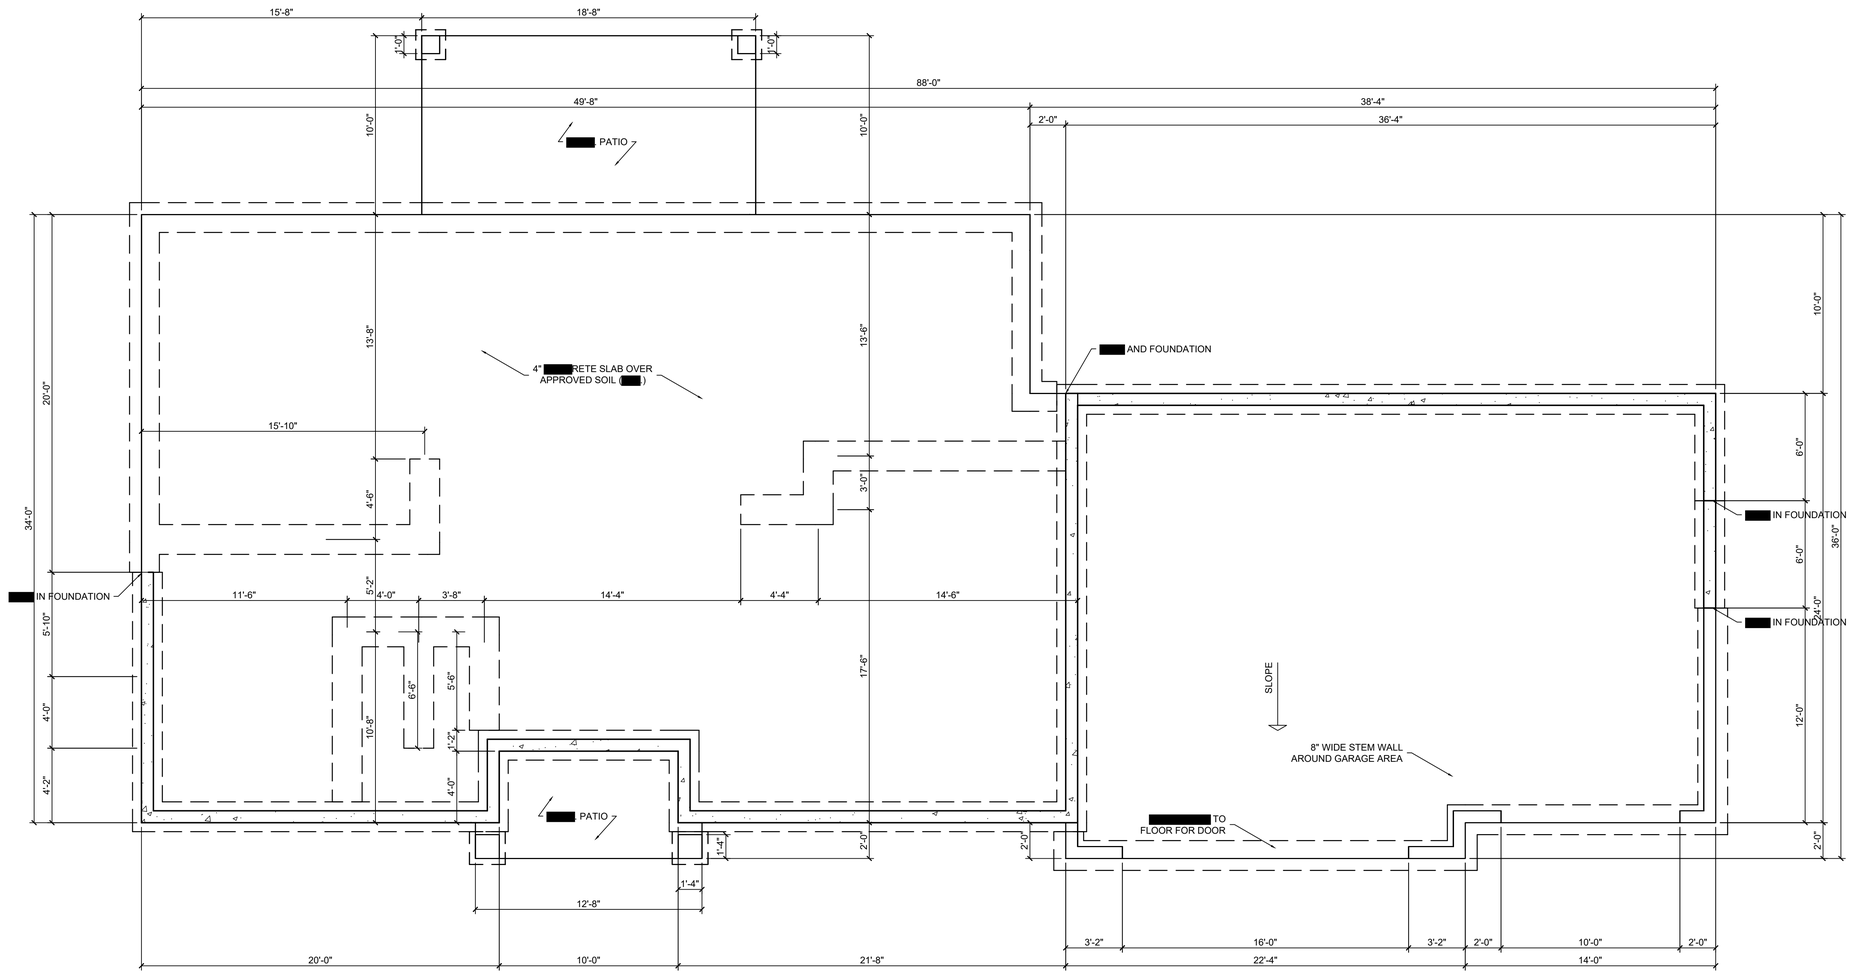

[redacted] PLAN

SCALE: ¼" = 1'-0"

DRAWN BY	JLF
PROJECT #	20-142
REV.1	-
REV.2	-
FINAL REV.	1/11/2021

COOPER RESIDENCE

[redacted] UT 84774

[redacted] PLAN

JLF J. LONNIE FOX DRAFTING AND DESIGN

phone (801) 287-1442 • jlonniefox@gmail.com • www.jlfdraftingdesign.com

BASEMENT SQFT	1713
MAIN FLR SQFT	1705
2ND FLR SQFT	0
GARAGE SQFT	909
TOTAL FIN SQFT	3418
TOTAL SQFT	3418

SHEET #

A1.1

COPYRIGHT 2020 J. LONNIE FOX DRAFTING AND DESIGN. THE [redacted] IS GRANTED A SINGLE USE LICENSE FOR CONSTRUCTION ONLY. THESE PLANS ARE COPYRIGHTED AND ARE SUBJECT TO COPYRIGHT PROTECTION AS AN "ARCHITECTURAL WORK" UNDER THE COPYRIGHT ACT.