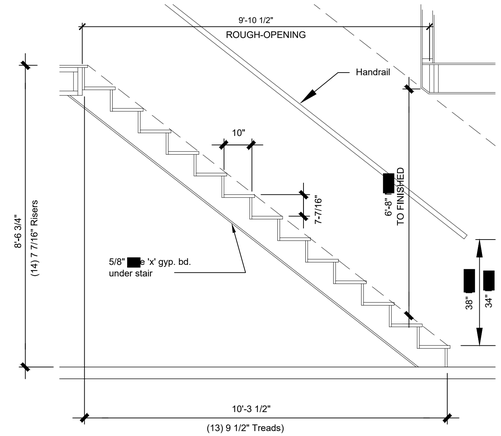

[redacted]. [redacted]

[redacted]: NTS

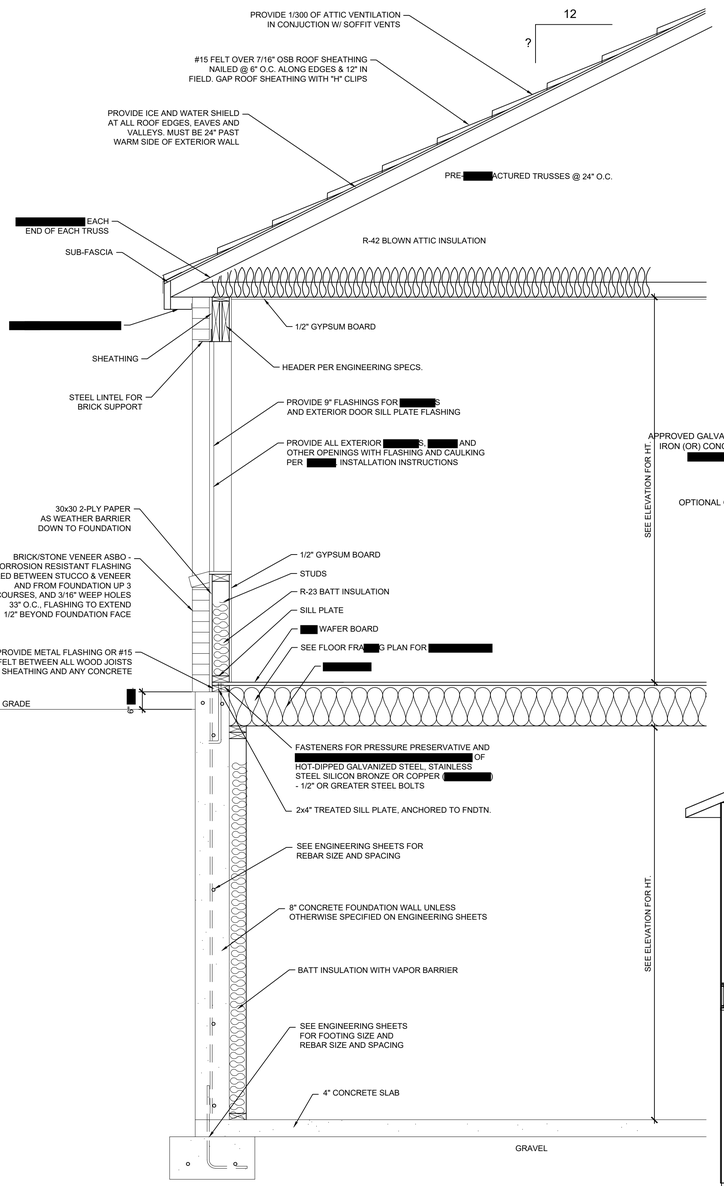

[redacted]. WALL SECTION [redacted]

[redacted]: ¾" = 1'-0"

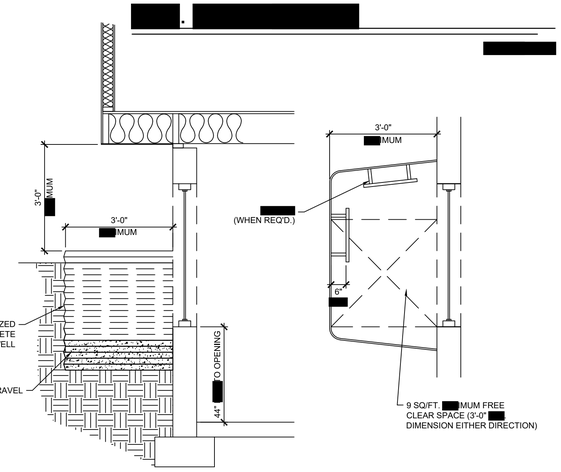

[redacted]. [redacted] WELL [redacted]

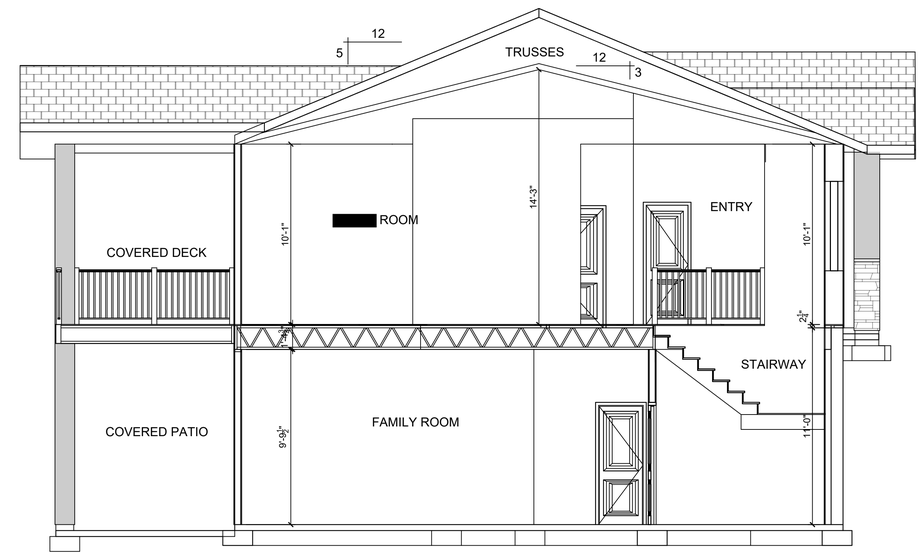

1 SECTION

SCALE: ¼" = 1'-0"

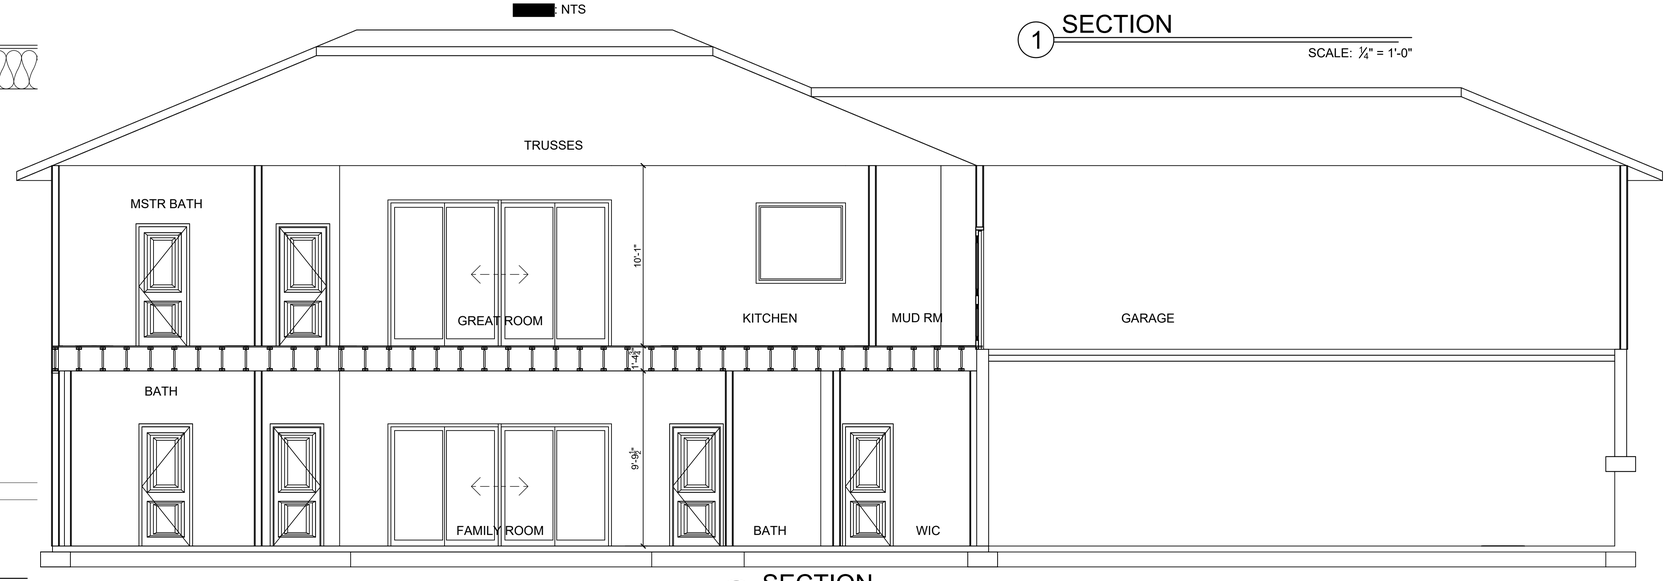

2 SECTION

SCALE: ¼" = 1'-0"

DRAWN BY	JLF
PROJECT #	20-142
REV.1	-
REV.2	-
FINAL REV.	1/11/2021

COOPER RESIDENCE

[redacted] UT 84774

BUILDING SECTIONS

J. LONNIE FOX
DRAFTING AND DESIGN
phone: (801) 487-1440 • jlonniefox@gmail.com • www.jlfdraftingdesign.com

BASEMENT SQ/FT	1713
MAIN FLR SQ/FT	1705
2ND FLR SQ/FT	0
GARAGE SQ/FT	909
TOTAL FIN SQ/FT	3418
TOTAL SQ/FT	3418

SHEET #

A3.1

COPYRIGHT 2020 J. LONNIE FOX DRAFTING AND DESIGN. THE [redacted] IS GRANTED A SINGLE USE LICENSE FOR CONSTRUCTION ONLY. THESE PLANS ARE COPYRIGHTED AND ARE SUBJECT TO COPYRIGHT PROTECTION AS AN "ARCHITECTURAL WORK" UNDER THE COPYRIGHT ACT.