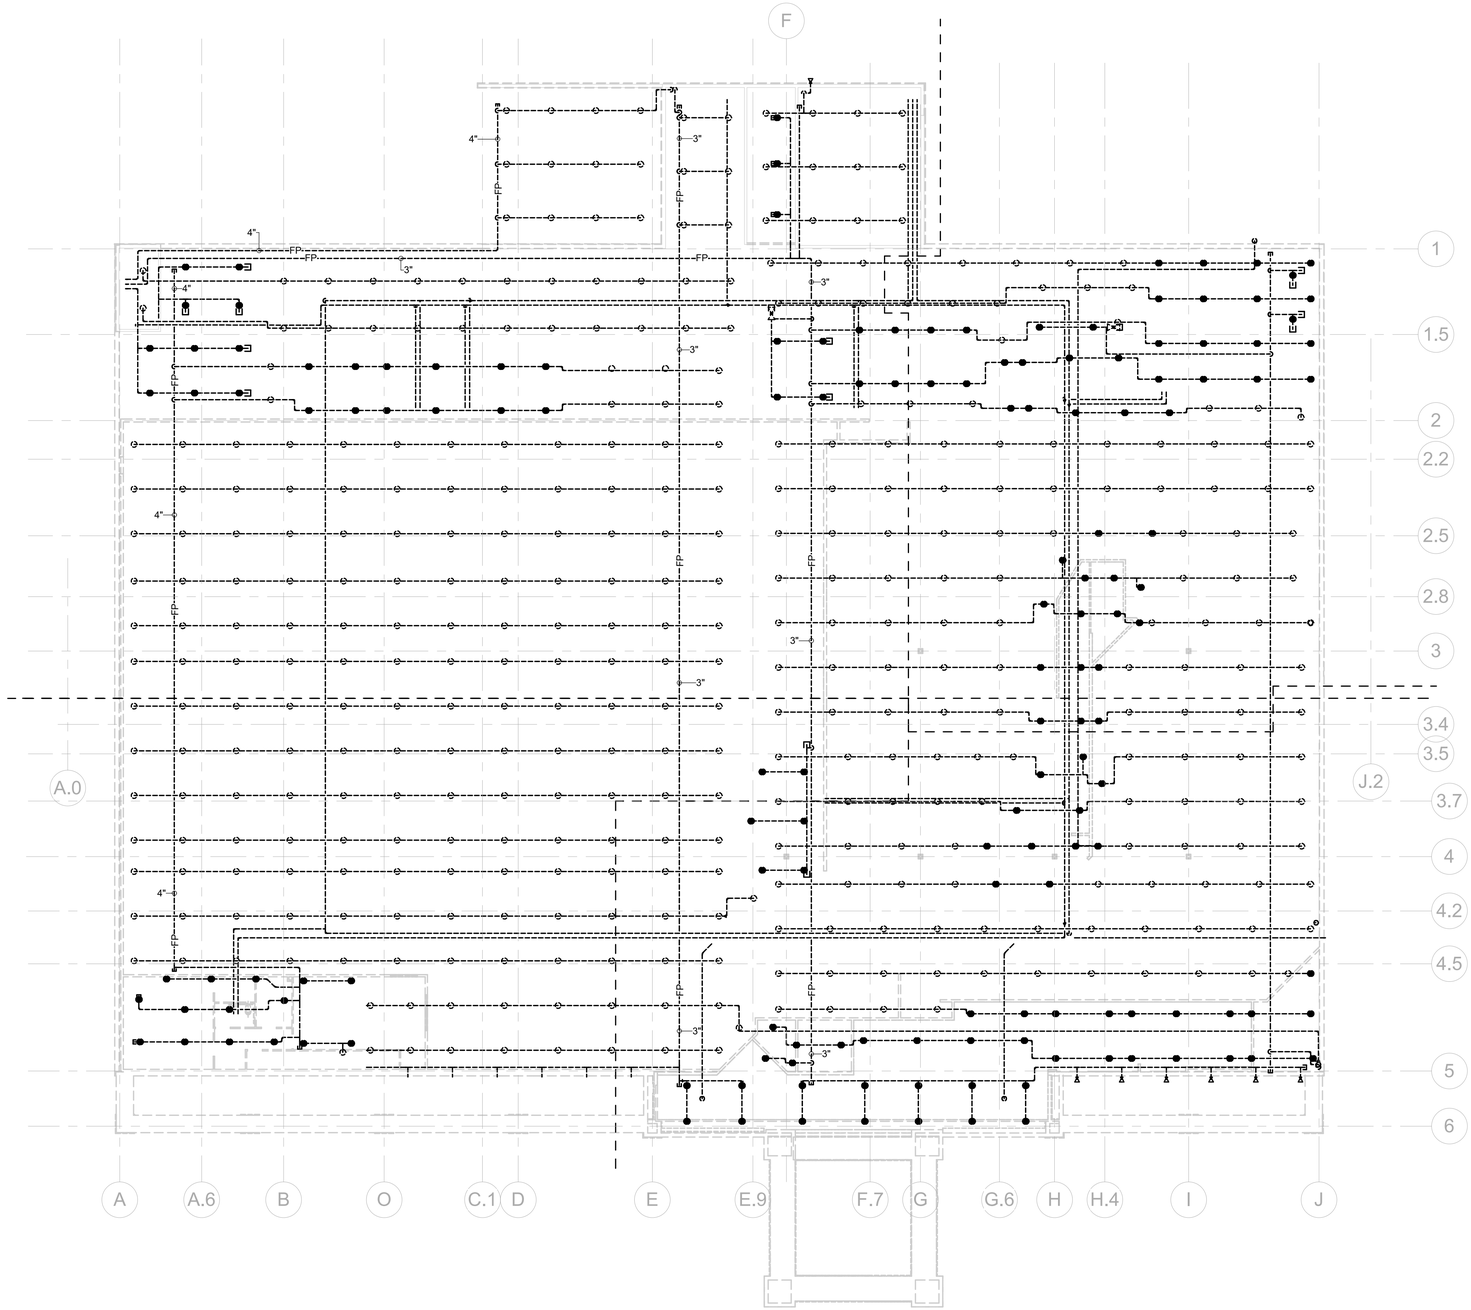

1 SECOND FLOOR REMOVAL PLAN

1/16" = 1'-0"

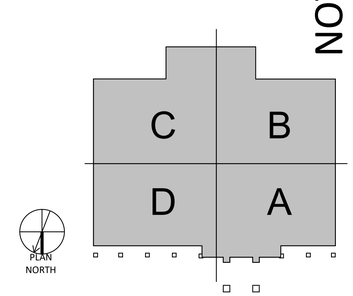

KEY PLAN

NOT FOR CONSTRUCTION

beardsley
architects + engineers

AUBURN
64 South Street
Auburn, NY 13021
315.253.7301

MALONE
320 West Main Street
Malone, NY 12953
518.483.1585

SYRACUSE
5789 Widewaters Pkwy
Dewitt, NY 13214
315.472.6980

EC4B engineering, p.c.
15 Schoen Place
Suite 300
Pittsford, NY 14534
Phone: (585) 641-7121
Fax: (585) 362-4175
www.ec4b.com

WARNING
Any alterations to this document not conforming to section 7307, New York State Education Law are strictly prohibited.

CONSTRUCTION DOCUMENTS
2/11/2022

Project Number: 18029

By: WAB
Designed By: NMG
Reviewed By: NMG

no.	revision description	by	date

SECOND FLOOR REMOVAL PLAN

Filename: C:\Users\jcapponelli\Documents\17159 - IGA SRMT MEP Central_jcapponelli.rvt
2/11/2023 3:35:56 PM
, Engineering, , ©